

STYLE B — ELEVATION & SECTION


Base to floor (1" clearance) · fringe header 7" AFF · 10" exposed face · rear plumb, inside face raked

MAGGIE O'NEIL — THE WILLARD · SCOTCH BAR CST-23

Rev to EST-2026-110 · Style B: 4 channels/half · 07/16/2026


ALL COM · R120" field verify · units separated — confirm vs 82" cap · pattern stylized

FRONT ELEVATION (DEVELOPED)

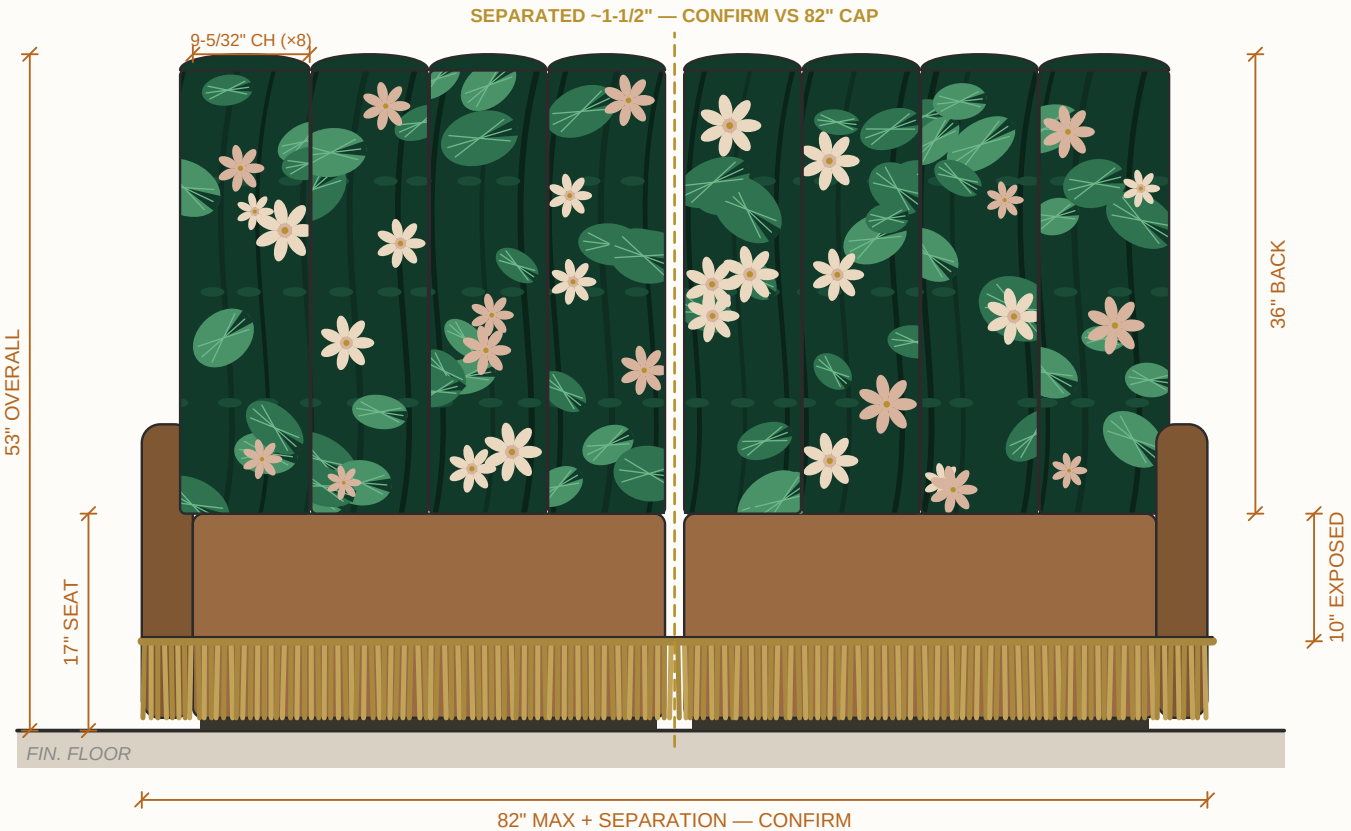

SIDE SECTION

rear plumb · inside face raked ~10°

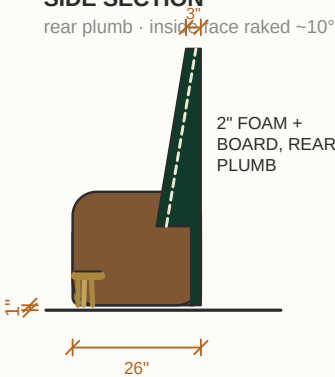


MATERIALS (ALL COM)

- NYPHEUS VELVET EMERALD**
GP&J Baker BP10814-2 · inside back
Not Cal TB 117 tested — client confirms FF&E
- VINTAGE ALE SVI001**
Keyston Bros · seat + face + arms
- RUPI 158 FRINGE**
Fabricut 6" · header 7" AFF · recalc yardage

STYLE B — FLOOR PLAN (TRUE R120")

Full-page dimensioned plan · arc lengths, chord, sagitta, radii · install reference

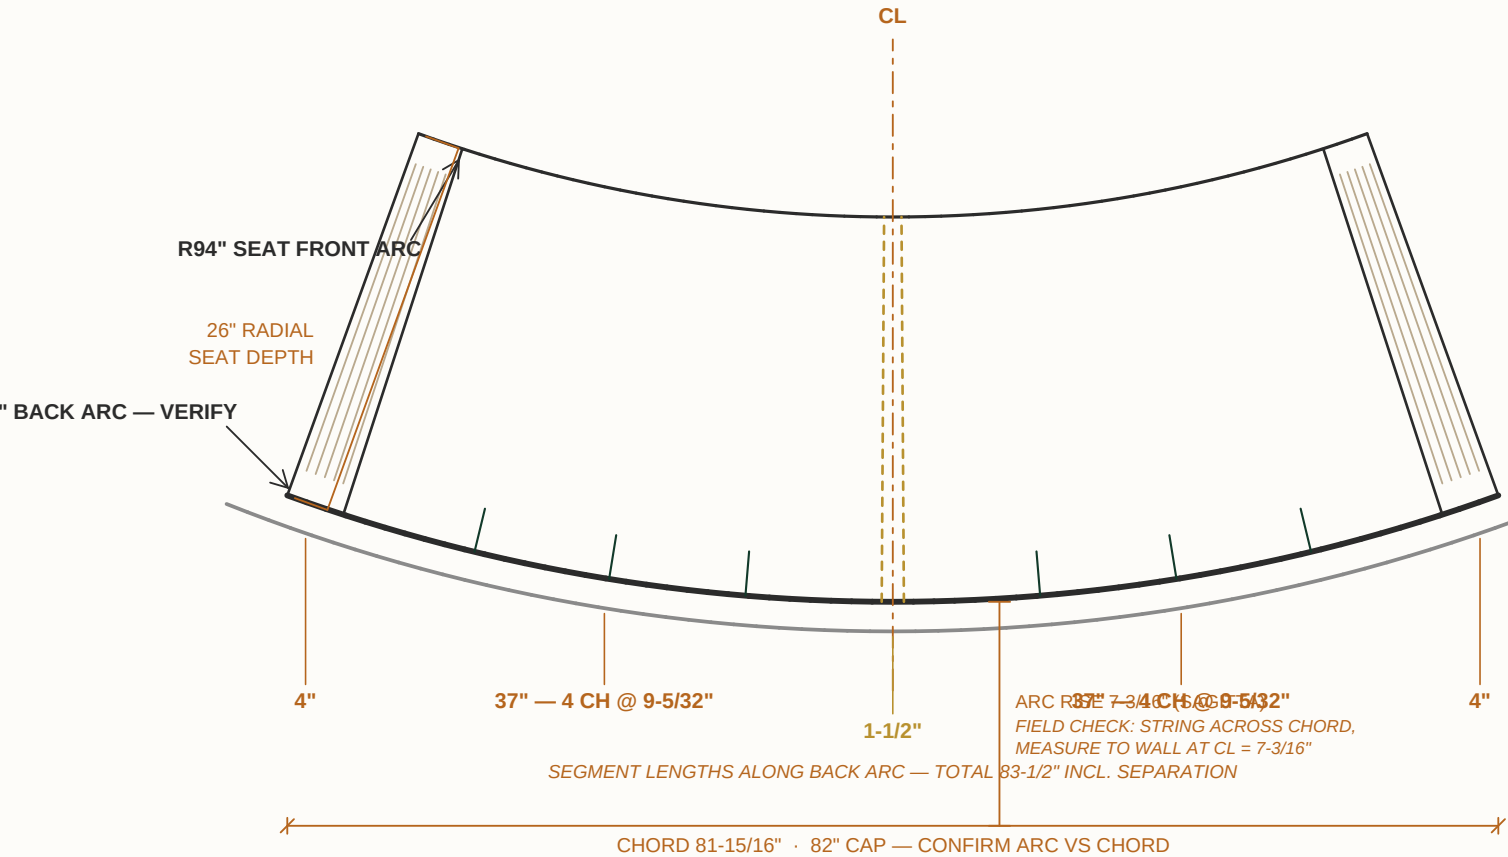

SEGMENT SCHEDULE

A1	Armrest	4"
U1	Bench half — 4 ch	37"
G	Separation	1-1/2"
U2	Bench half — 4 ch	37"
A2	Armrest	4"
TOTAL (arc)		83-1/2"

83-1/2" > 82" CAP — RESOLVE:

- a) butt-joint units (no gap) = 82" exact, or
- b) shrink halves to 36-1/4" each w/ gap, or
- c) confirm cap is chord (81-15/16" OK as drawn)

INSTALL NOTES

- Units delivered separately; join at CL
- Maintain 18" min clearance to tables
- Rear plumb to wall — scribe to field curve
- Concealed glides · 1" floor clearance
- SCALE ≈ 1-1/4" = 1'-0" at full-size print

FACE OF WALL
FIELD VERIFY CURVATURE

STYLE B — ISOMETRIC (3D MODEL RENDER)

Depth-sorted parametric model — Empire Presentation 3D Pipeline v1

MAGGIE O'NEIL — THE WILLARD · SCOTCH BAR CST-23

Rev to EST-2026-110 · Style B: 4 channels/half · 07/16/2026

ALL COM · R120" field verify · units separated — confirm vs 82" cap · pattern stylized



KEY DIMENSIONS

82" cap: 4 + 37 + 37 + 4 (+ gap — see plan)
17" seat · 36" back · 53" overall
26" radial depth · base to floor, 1" clr
Wedge back: 9" seat → 3" top · rear plumb
Fringe header 7" AFF · 10" exposed face
8 channels @ 9-5/32"

ALL COM · flammability confirm pending